


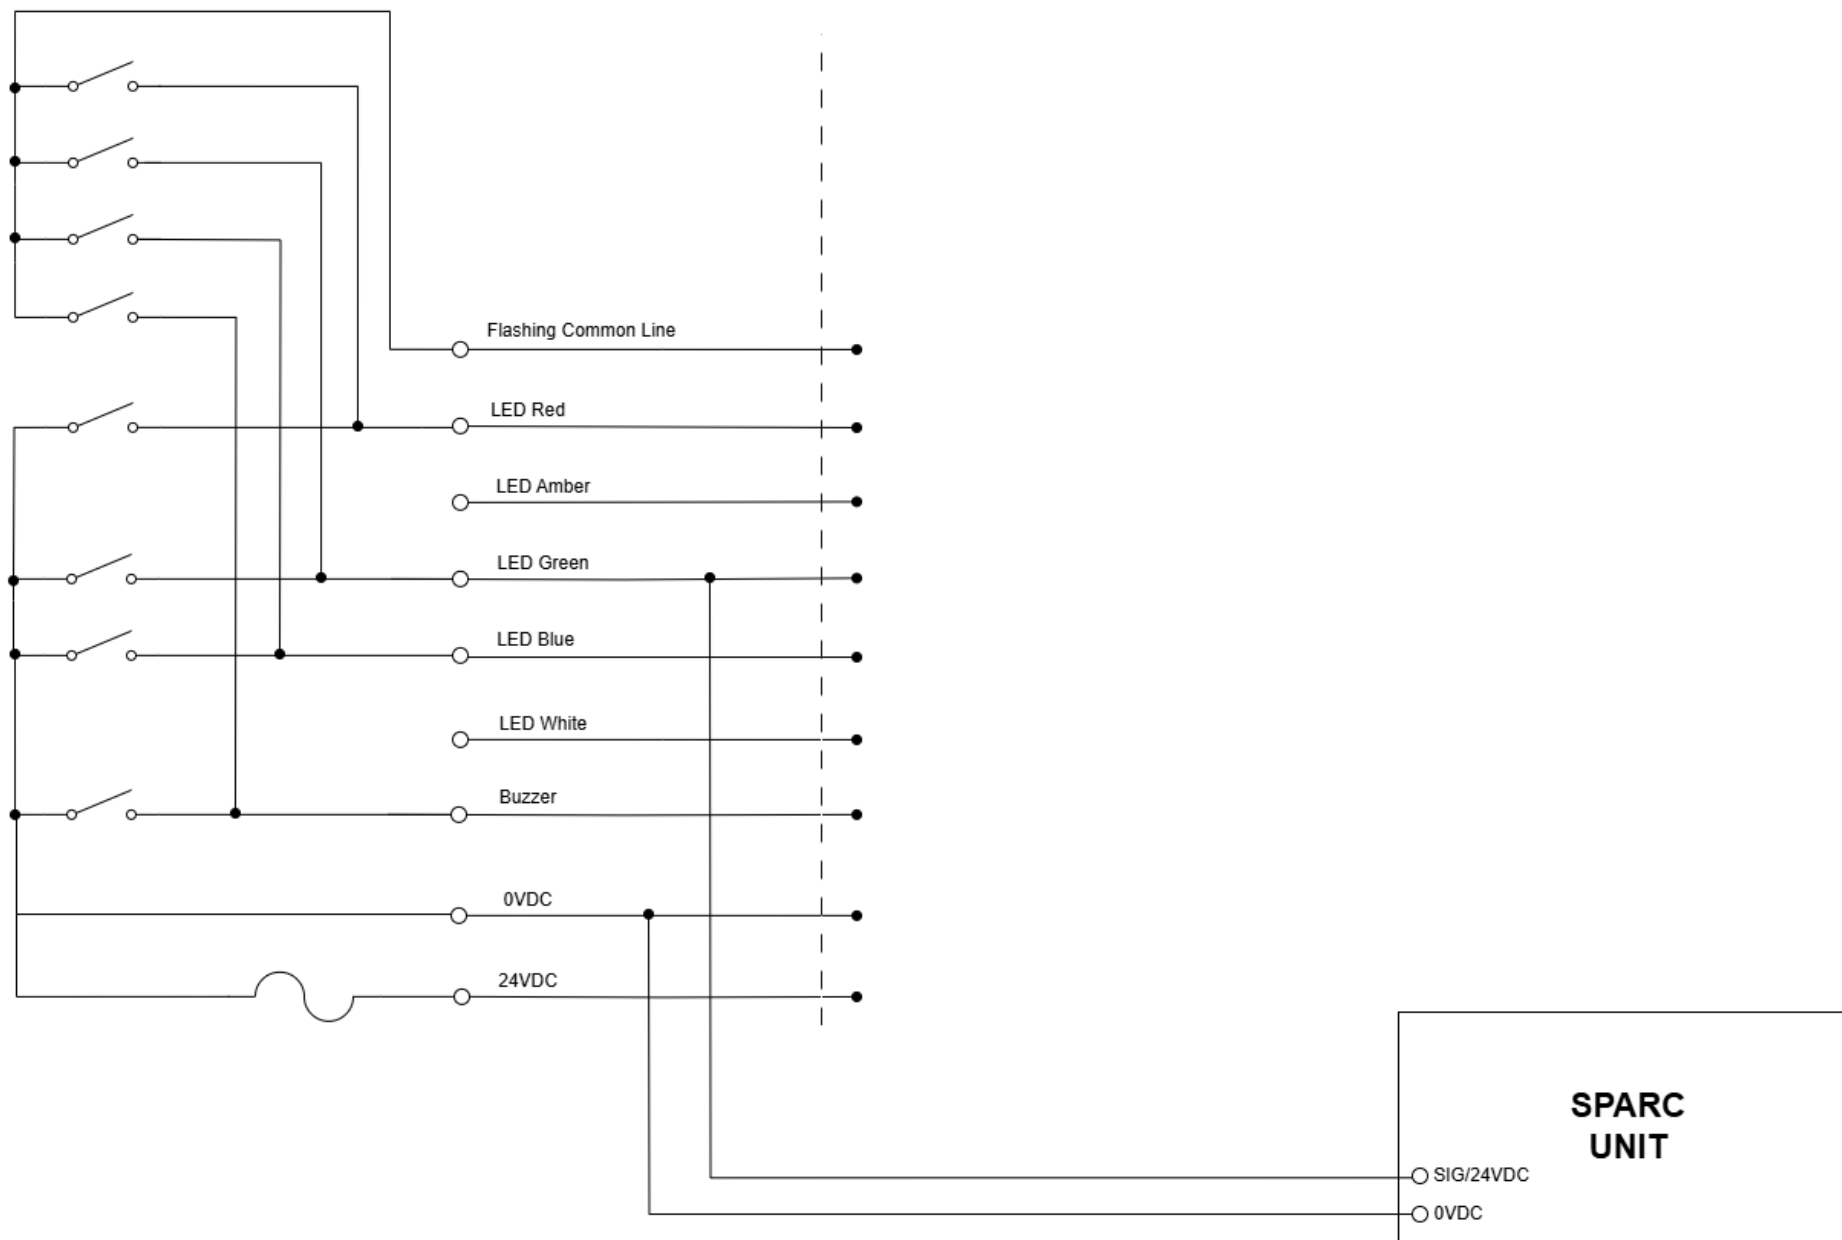

METRONARC
TECHNOLOGY

1 North Bridge Road #18-06 High Street Centre,
Singapore, 179094

TITLE:

SPARC CNC Installation Wiring Diagram

Product: Sparc CNC

Date: 11-20-2024

A4