
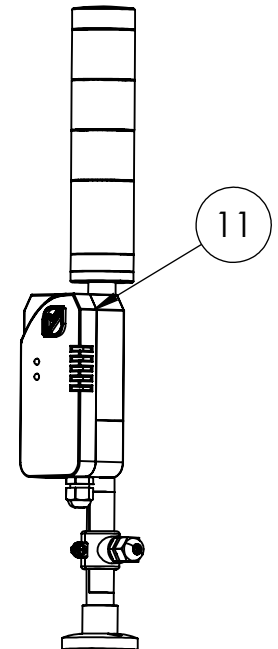
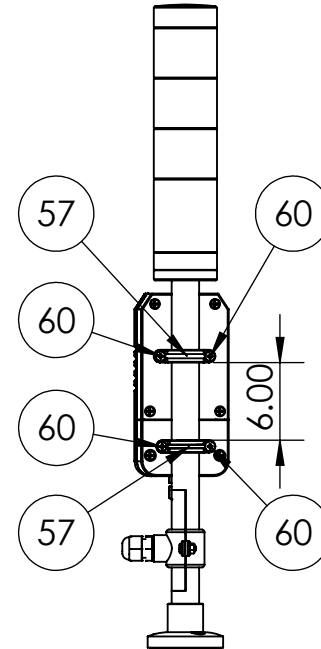
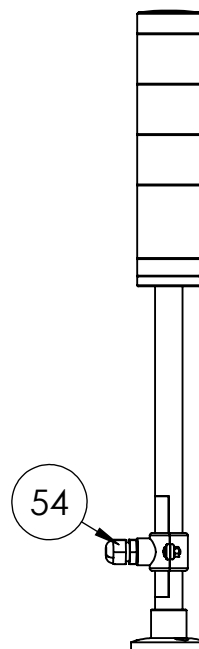
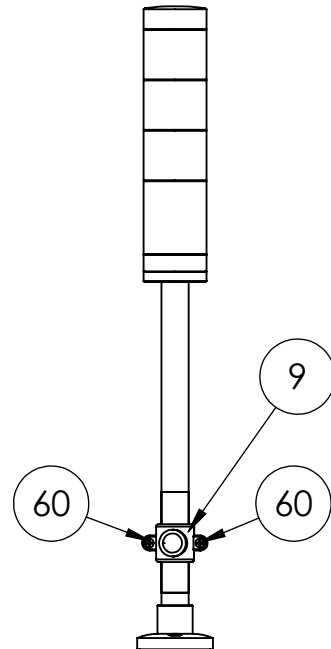


BILL OF MATERIALS

MATERIAL CODE	DESCRIPTION	MATERIAL	UNIT	QUANTITY
9	SPARC T-CONNECTION	PLA+	EA	1
11	SPARC	PLA+	EA	1
54	3/4 INCH OMEGA CLAMP	SS304	EA	2
57	PG9 CABLE GLAND	PA66	EA	1
60	M4 BOLT, NUT AND WASHER	SS304	EA	AS REQUIRED

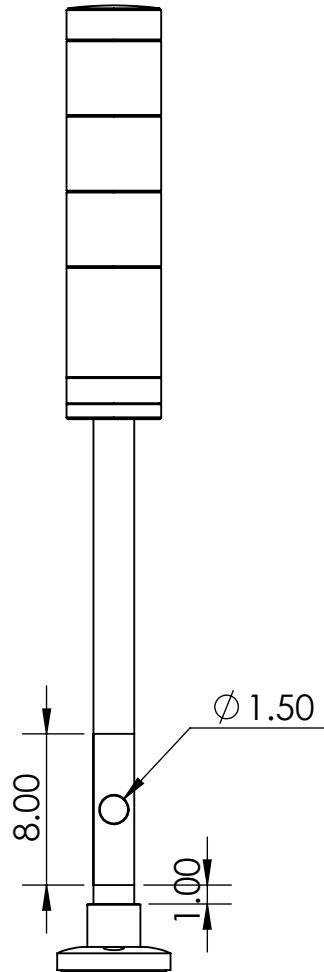

NOTES:

1. UNITS ARE IN CM

						PT. RONSTAN INTERNATIONAL			
3	10-JAN-2025	RDP	RR	RR	ISSUED FOR CONSTRUCTION				
2	05-DEC-2024	RDP	RR	RR	RE-ISSUED FOR REVIEW				
1	04-DEC-2024	RDP	RR	RR	ISSUED FOR REVIEW	Title TOWER LAMP SPARC INSTALLATION			
Rev	Date	Drawn	Chkd	Appr	Description				
 METRONARC TECHNOLOGY 1 North Bridge Road #18-16 High Street Center Singapore, 179094						Scale NTS	Size A3	Drawing no. MTR-056-002A-03	Rev. 03