


MATERIAL CODE	DESCRIPTION	MATERIAL	UNIT	QUANTITY
10	SPARC BRACKET	PLA+	EA	1
11	SPARC	PLA+	EA	1
57	PG9 CABLE GLAND	PA66	EA	1
61	M5 BOLT, NUT AND WASHER	SS304	EA	AS REQUIRED

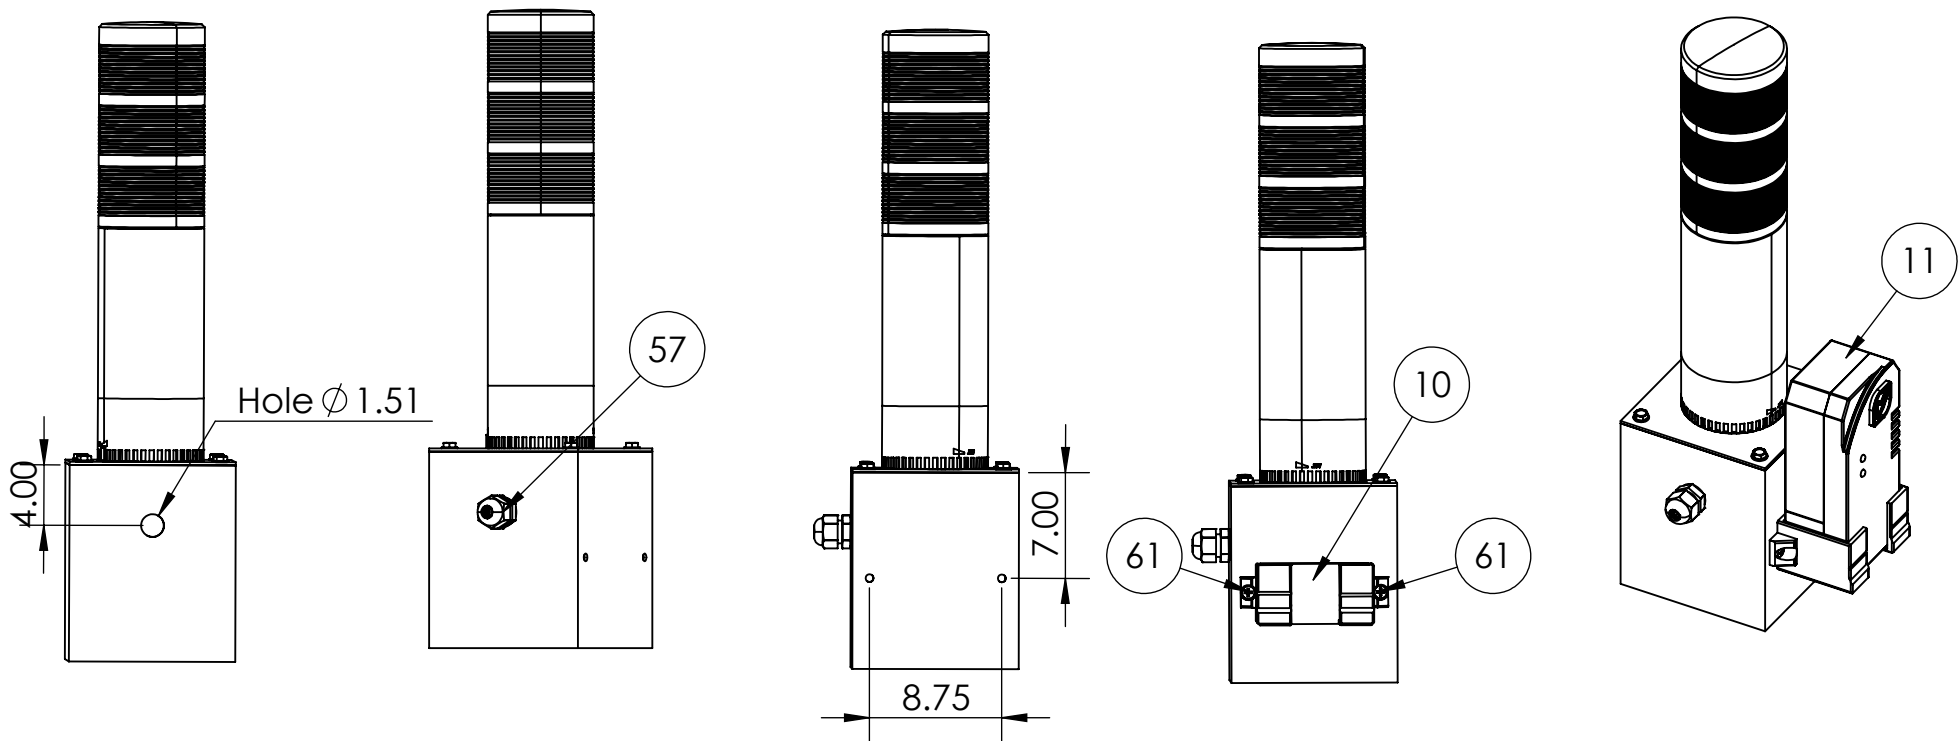

3	10-JAN-2025	RDP	RR	RR	ISSUED FOR CONSTRUCTION
2	05-DEC-2024	RDP	RR	RR	RE-ISSUED FOR REVIEW
1	18-DEC-2024	RDP	RR	RR	ISSUED FOR REVIEW
Rev	Date	Drawn	Chkd	Appr	Description

Title	TOWER LAMP SPARC INSTALLATION
-------	-------------------------------



1 North Bridge Road #18-16 High Street Center
Singapore, 179094

Scale	Size	Drawing no.	Rev.
NTS	A3	MTR-056-002B-03	03